


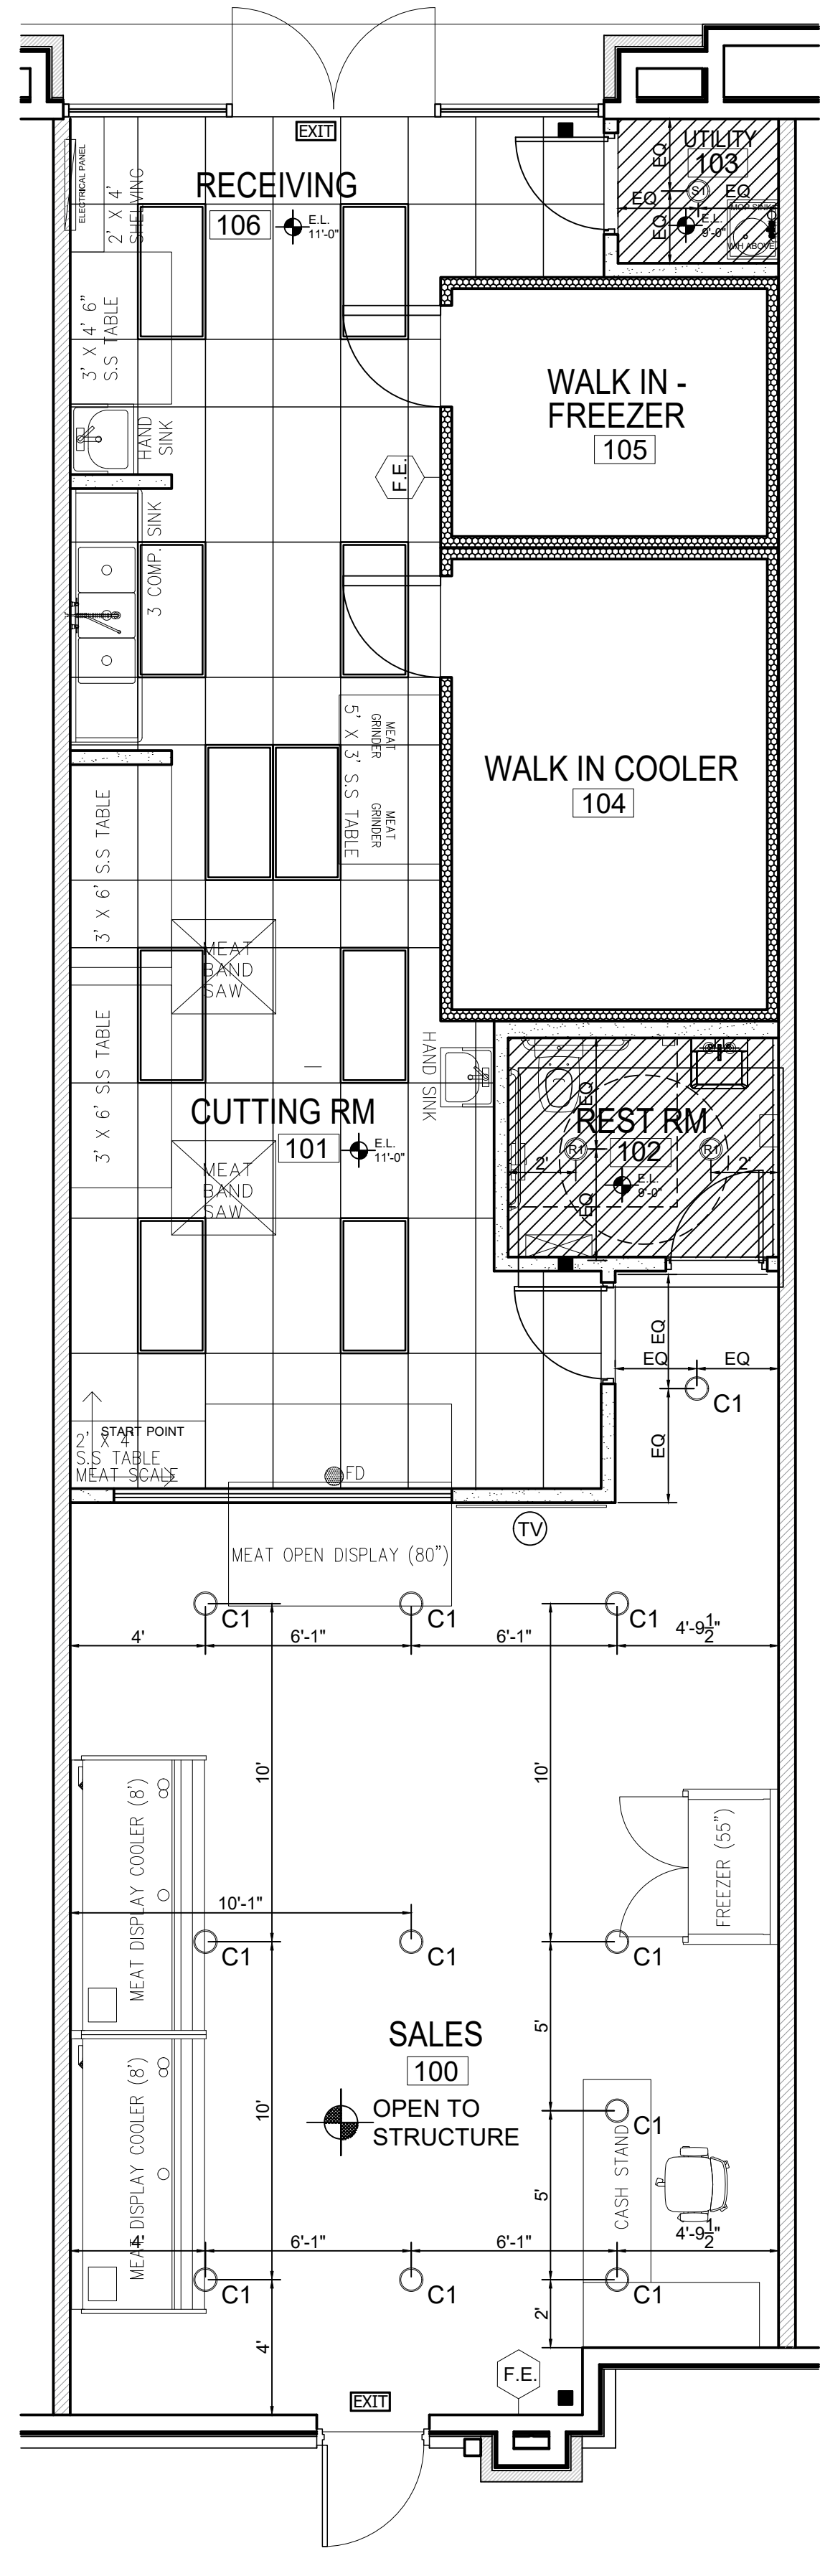

01 REFLECTED CEILING PLAN
SCALE: 1/4" = 1'-0"

CEILING LEGEND		
TAG	TYPE	SPECIFICATION
(R)	5" LED RECESSED DOWNLIGHT	Lithonia Lighting Model # 5G1BN LED M, 5 in. Brushed Nickel LED Recessed Downlighting Gimbale Module
(S)	7.25" LED FLUSH MOUNTLIGHT	Progress Lighting - P8222 Series 7.25 inch LED Flush Mount Wet Location Model # P8222-28-30K
(V)	VANITY LIGHT	Quozel Kolt 6" High Brushed Nickel LED Wall Sconce Available at lampsplus, Style # 18C22
(EXIT)	ILLUMINATED EXIT SIGN	REFERENCE ELECTRICAL DRAWINGS FOR DETAILS
(G)	GYPSTUM BOARD	5/8" GYPSTUM BOARD CEILING SEMIGLOSS PAINT, WHITE/level 4 SMOOTH FINISH CEILING HEIGHT AS MENTIONED IN THE ROOMS. PAINT FINISH- REFER ROOM FINISH SCHEDULE
(C)	CYLINDER LIGHT	WARELIGHT - 6" LED Architectural Cylinder Light Fixture 2200 Lumens, 25W, CCT Selectable, 120-277V, Black Finish ITEM: WL-CYL6-25W-SCT-0-10V-UNV-S-BK
(L)	2' X 4" RECESSED LIGHT FIXTURE	LITHONIA LIGHTING, SERIES 2ESL4, 2' X 4" LED LIGHTING REFERENCE ELECTRICAL DRAWINGS FOR DETAILS
(I)	2' X 4" LAY-IN	USG, ASTRO ACOUSTICAL PANEL, CLIMA PLUS ITEM NO. 8243, FINE TEXTURED, WHITE SLT SHADOW LINE REGULAR OR EQUAL. GRID: USG Donn® Brand DX®/DXL™ 15/16" Acoustical Suspension System, FLAT WHITE PROVIDE IN KITCHEN AREAS.
(O)	OPEN TO STRUCTURE	OPEN TO STRUCTURE CEILING

GENERAL NOTE:
1. CENTER LIGHT FIXTURES IN ROOMS UNLESS NOTED OTHERWISE.
2. KEEP HT. OF THE SALES AREA LIGHT FIXTURES AT 9'-0" FROM THE FFL. VERIFY HEIGHTS WITH THE OWNER ALSO.
3. KEEP EXTERIOR LIGHT FIXTURES AS IS REPAIR IF NEEDED AND REPLACE LIGHT BULBS IF NEEDED.



ROOM FINISH LEGEND							
FLOORING AND BASE							
CODE	MATERIAL	MANUFACTURER	PRODUCT NO.	COLOR	FINISH	DIMENSIONS	REMARKS
CT-1	CERAMIC TILES	PIANETTO MORANDI WHITE POLISHED PORCELAIN	SKU: 100894758 AT FLOOR & DECOR	WHITE	POLISHED/ HIGH GLOSS	24"x48"	- PROVIDE IN SALES RM 100 - TILE BASE - WB-1A - TO MATCH WITH FLOOR TILE PROVIDE IN SALES
CT-2	CEMENTITIOUS URETHANE SEAMLESS FLOORING SYSTEM SAND BROADCAST W/ CONTROL & EXPANSION JOINTS	RES-TEK FLOOR SYSTEMS	PUR-GUARD HD-SL	P-22 DARK GRAY	MATTE SOLID COLOR FINISH	-	- PROVIDE IN CUTTING RM 101, RECEIVING 106 AND 103 - BASE - PUR-GUARD HD-CS COVE BASE TO MATCH W/ FLOORING SYSTEM RES-TEK Acrylic Flooring & Concrete Repair Solutions Porton Schmucker Regional Sales Manager, Texas c: 972.922.6708 e: porton.schmucker@res-tek.net w: www.res-tek.net a: 110 Riverside Drive, Cartersville, GA 30120
CT-3	CERAMIC TILES	CORTA GRAY CERAMIC TILE	SKU: 100823459 AT FLOOR & DECOR	GRAY	MATTE	15"x30"	- PROVIDE IN RESTROOM 102 - TILE BASE - WB-3A - TO MATCH WITH WALL TILE PROVIDE IN RESTROOM - TILE GROUT - LATITRETE - STORMY GREY COLOR, PROVIDE ON RESTROOM FLOOR

CEILING							
CODE	MATERIAL	MANUFACTURER	PRODUCT NO.	COLOR	FINISH	DIMENSIONS	REMARKS
REF A4.0	ACOUSTICAL TILES	LAURENTO GRAY II POLISHED PORCELAIN TILE	SKU: 10079883 AT FLOOR & DECOR	GRAY	MATTE	24"x24"	USG, ASTRO ACOUSTICAL PANEL, CLIMA PLUS ITEM NO. 8243, FINE TEXTURED, WHITE SLT SHADOW LINE REGULAR OR EQUAL. REFER TO REFLECTED CEILING PLAN SHEET - AS.0
REF A4.0	ACOUSTICAL TILES	LAURENTO GRAY II POLISHED PORCELAIN TILE	SKU: 10079883 AT FLOOR & DECOR	GRAY	MATTE	24"x24"	USG, ASTRO ACOUSTICAL PANEL, CLIMA PLUS ITEM NO. 8243, FINE TEXTURED, WHITE SLT SHADOW LINE REGULAR OR EQUAL. REFER TO REFLECTED CEILING PLAN SHEET - AS.0
REF A4.0	GYPSTUM BOARD	-	-	WHITE	SEMI GLOSS	-	5/8" GYPSTUM BD CEILING SEMIGLOSS PAINT WHITE COLOR
REF A4.0	OPEN TO STRUCTURE	-	-	-	-	-	OPEN TO STRUCTURE CEILING IN SALES AREA 100


WALLS							
CODE	MATERIAL	MANUFACTURER	PRODUCT NO.	COLOR	FINISH	DIMENSIONS	REMARKS
PT-1A	INTERIOR PAINT TYPE 1	SHERWIN WILLIAMS	PER OWNER	PER OWNER	EGG SHELL	N/A	PER OWNER - ON ALL WALLS
PT-1B	INTERIOR PAINT TYPE 1	SHERWIN WILLIAMS	PER OWNER	PER OWNER	EGG SHELL	N/A	PER OWNER - ON ALL WALLS
CT-1A	WALL TILE TYPE 1	FESTIVAL	BRIGHT WHITE ICE CERAMIC TILE	WHITE	SMOOTH	4"x10"	PER OWNER - ON RESTROOM WALLS; REFER SHEET AS.0 FOR ELEVATION HT. AVAILABLE AT FLOOR & DECOR; SKU: 100112689
CT-3A	WALL TILE TYPE 3	ADESSI ASTRID GRIGIO CERAMIC WALL TILE	SKU: 100833144 AT FLOOR & DECOR	-	MATTE	12"x35"	PER OWNER - ON RESTROOM MAIN WALL ONLY; REFER SHEET AS.0 FOR ELEVATION HT. AVAILABLE AT FLOOR & DECOR; SKU: 100833144
FRP	FIBER REINFORCED PLASTIC UPTO CEILING	MARLITE	PEBBLED P145 SILVER	-	-	-	IN CUTTING RECEIVING AND UTILITY RM UPTO FINISHED CEILING

- NOTES:
1. ALL WALLS SHALL RECEIVE LEVEL 3 SMOOTH DRYWALL FINISH.
 2. ALL PAINT COLOR ARE SUBJECT TO APPROVAL BY THE OWNER AND DESIGN TEAM PRIOR TO APPLICATION. G.C. TO MAKE 2' X 2' MOCK UP FOR APPROVAL.
 3. ALL MATERIALS IN FINISH SCHEDULE ARE CONTRACTOR SUPPLIED UNLESS NOTED OTHERWISE.
 4. CONTRACTOR TO REVIEW AND PREAPPROVE PAINT COLORS WITH THE OWNER PRIOR TO PURCHASING THEM.
 5. ALL INTERIOR WALLS TO BE SMOOTH DRYWALL WITH EGG-SHELL FINISH. CEILINGS TO HAVE SMOOTH DRYWALL WITH FLAT PAINT FINISH. CONTRACTOR TO REVIEW WALL SHEENS WITH THE OWNER PRIOR TO APPLICATION.
 6. CONTRACTOR TO PROVIDE SUBMITTALS AND (SAMPLING IF POSSIBLE) OF ALL FINISH MATERIALS TO THE OWNER FOR THEIR APPROVAL PRIOR TO ORDERING AND INSTALLATION.

- NOTE: 1. CONTRACTOR TO SHOW THE PAINT MOCK-UP TO THE OWNER AND SEEK APPROVAL PRIOR TO ORDERING AND PERFORMING PAINTWORK.
2. CONTRACTOR TO SHOW THE FLOORING MOCK-UP TO THE OWNER AND SEEK APPROVAL PRIOR TO ORDERING AND INSTALLATION.

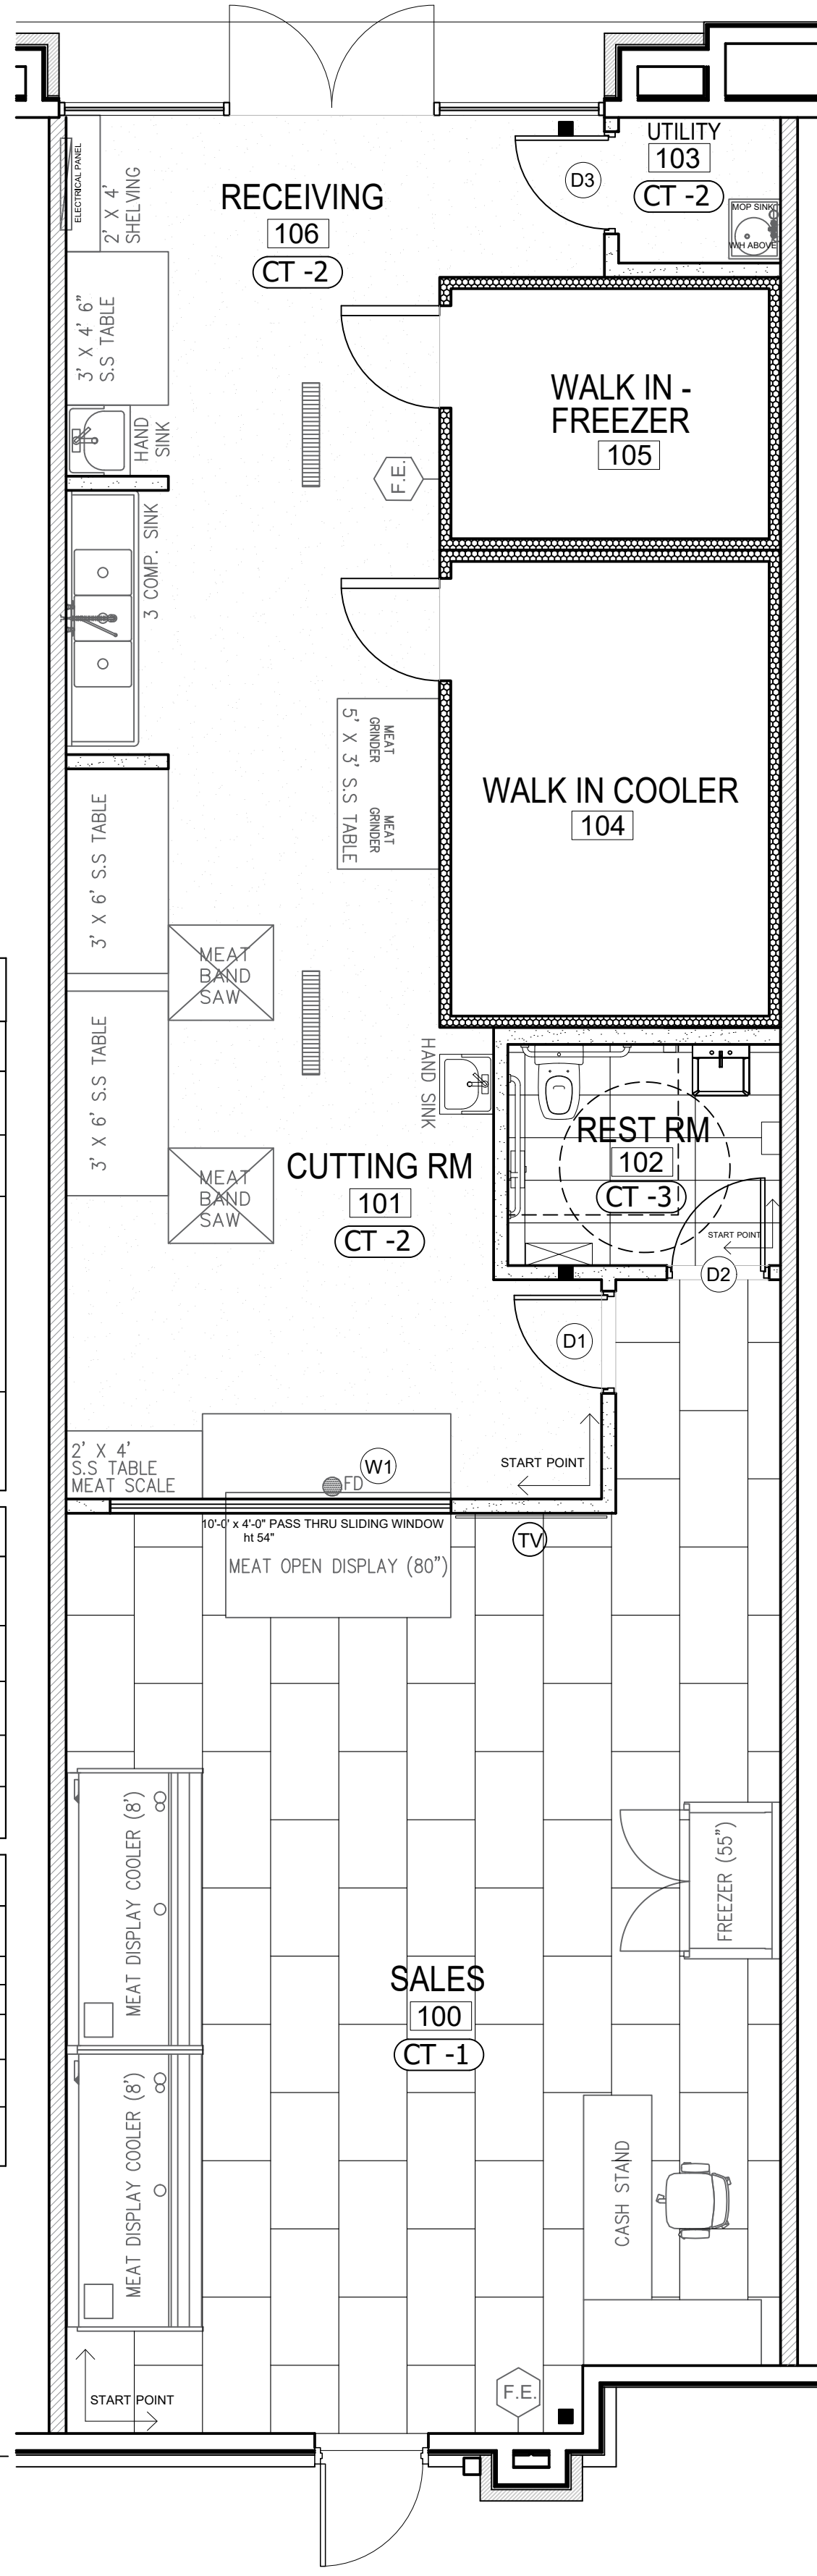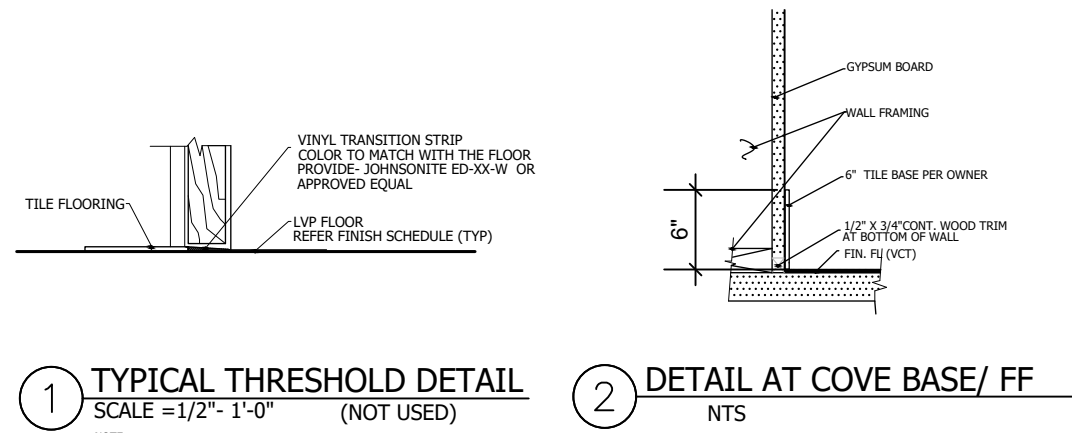

02 RM FINISH PLAN
SCALE: 1/4" = 1'-0"

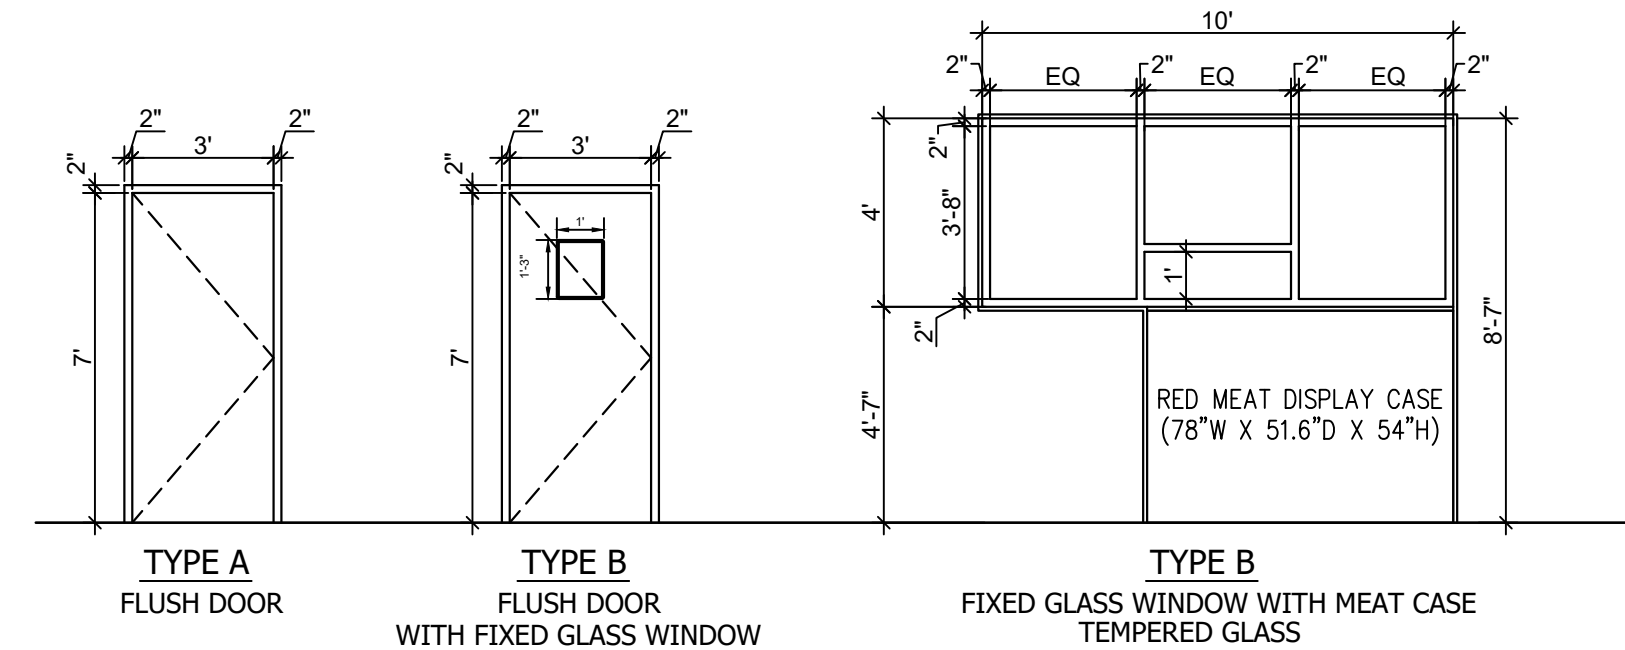

SCALE = 1/4"-1'-0"


DOOR SCHEDULE												
DOOR NO.	NEW/EXIST	TYPE	MATL	WIDTH	HEIGHT	THICK	FINISH	MAT'L	FINISH	FIRE RATING	HDW SETS	DETAILS
D1	NEW	B	PBC	3'-0"	7'-0"	1-3/4"	LAMINATE/ GLASS LITE	AL	DARK BRONZE	-	1	-
D2	NEW	A	PBC	3'-0"	7'-0"	1-3/4"	LAMINATE	AL	DARK BRONZE	-	4	-
D3	NEW	A	PBC	3'-0"	7'-0"	1-3/4"	LAMINATE	AL	DARK BRONZE	-	1	-

ABBREVIATIONS: PBC = PARTICLE BOARD CORE DOOR, AL = ALUMINUM; SF= SIDELITES

DOOR LAMINATE FINISH- WILSONART STANDARD HPL FINISH
FINNACLE WALNUT 7992-38
Fine Velvet texture


WINDOW SCHEDULE						FRAME							
NO.	NEW/EXIST	TYPE	DOOR TYPE	MEASUREMENTS	FINISH	MAT'L	FINISH	FIRE RATING	HDW SETS	DETAILS			NOTES
										HEAD	JAMB	SILL	
W1	NEW	B	-	SEE ELEVATIONS	TEMPERED GLASS	AL	PAINTED TBD	-	-	-	-	-	SEE ELEVATIONS

HARDWARE SETS	
PROVIDE ALL LOCKSETS AND HINGES SATIN NICKEL FINISH	
HARDWARE SET # 1 (TYPICAL OFFICE - KEYED LOCK)	HARDWARE SET # 4 (RESTROOM DOOR)
1 OFFICE LOCKSET 4 HINGES 1 ACOUSTIC SEAL FLOOR DOOR STOP WALL MOUNTED FLUSH BUMPER BALDWIN 1-3/4" DIA #425214	1 COAT HOOK 1 PRIVACY DOOR LEVER SET 1 PUSH PLATE - 1 PULL BAR 4 HINGES 1 ACOUSTIC SEAL 1 KICK PLATE (PUSH SIDE ONLY)- 8"x34" FLOOR DOOR STOP WALL MOUNTED FLUSH BUMPER

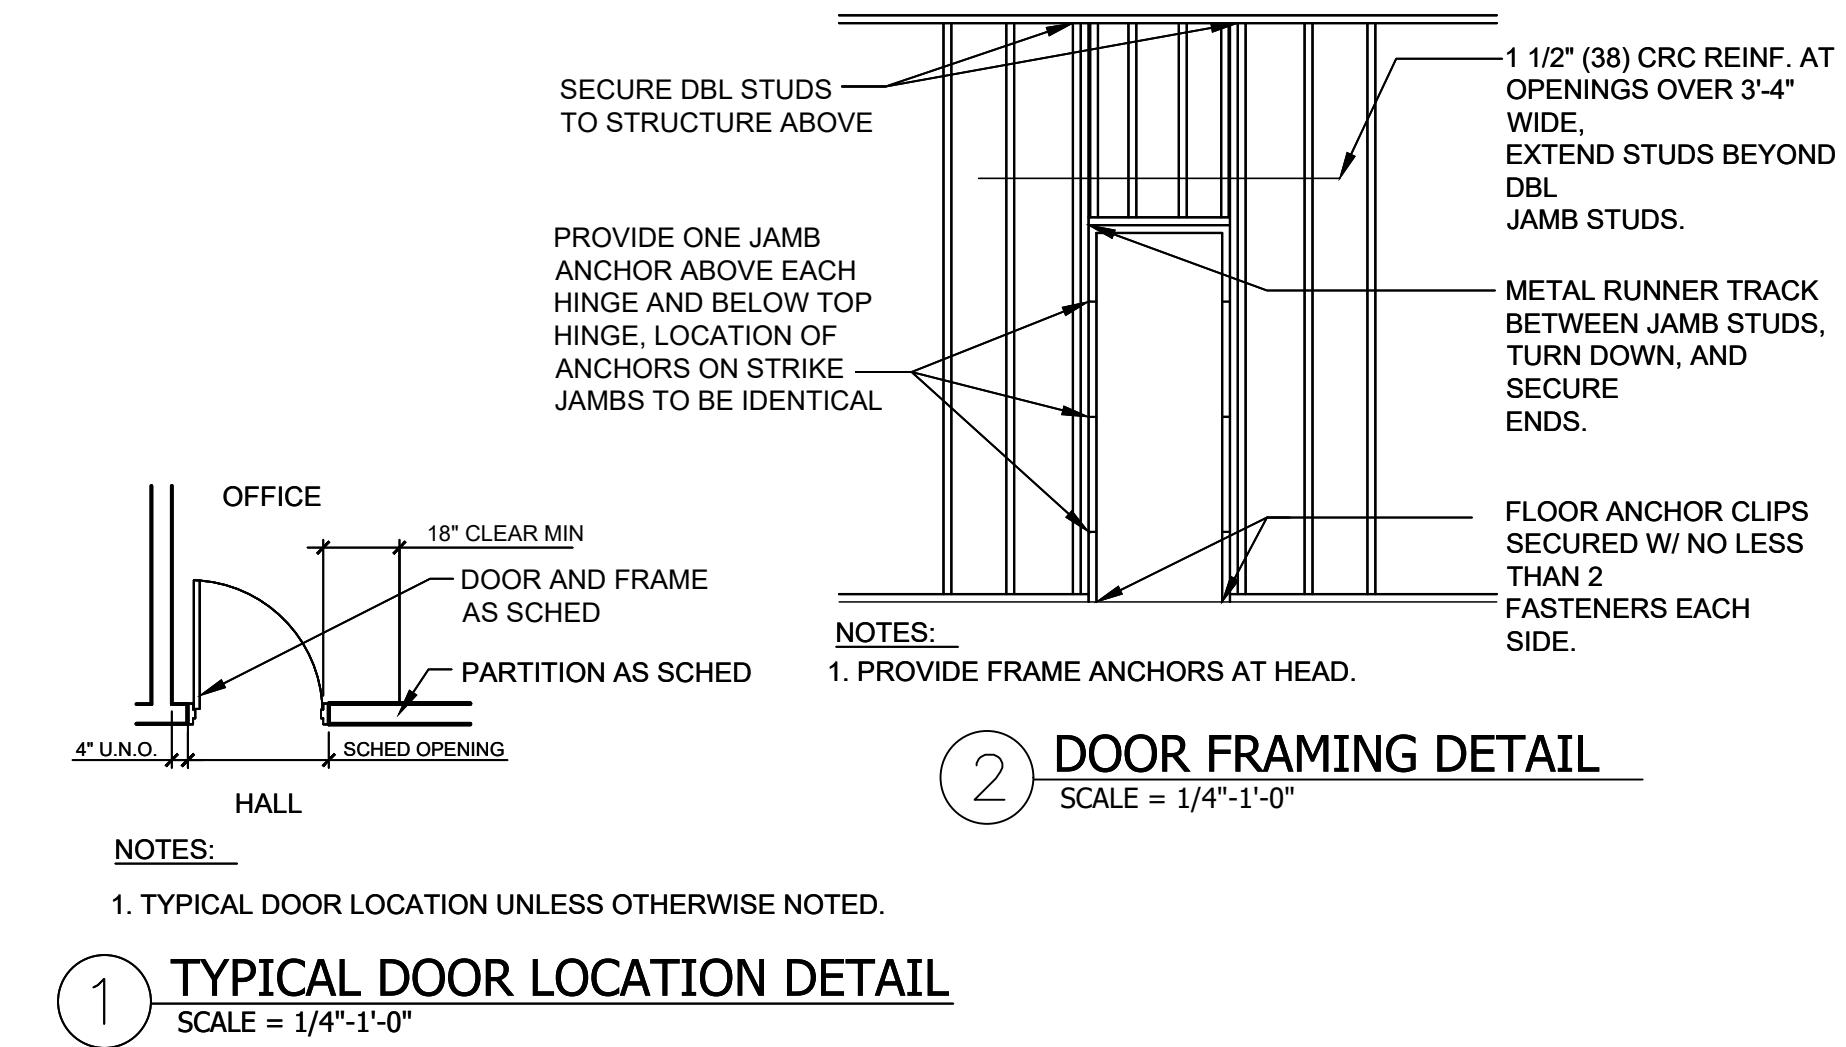

- DOOR NOTES :
1. ALL EXTERIOR DOORS WITH FRAMES ARE TO BE INSULATED, U.N.O.
 2. FIELD VERIFY ALL ROUGH OPENINGS PRIOR TO SUBMITTING SHOP DRAWINGS.
 3. THRESHOLDS AT DOORWAYS SHALL NOT EXCEED 1" IN HEIGHT. RAISED THRESHOLDS AND FLOOR LEVEL CHANGES AT ACCESSIBLE DOORWAYS SHALL BE BEVELED WITH A SLOPE NO GREATER THAN 1:2. DOOR HARDWARE, HANDLES, PULLS, LATCHES, LOCKS AND OTHER OPERATING DEVICES ON ACCESSIBLE DOORS SHALL HAVE A SHAPE THAT IS EASY TO GRASP WITH ONE HAND AND DOES NOT REQUIRE TIGHT GRASPING, TIGHT PINCHING OR TWISTING OF THE WRIST TO OPERATE. LEVER OPERATED MECHANISMS, PUSH-TYPE MECHANISMS AND U-SHAPED HANDLES ARE ACCEPTABLE DESIGNS. HARDWARE REQUIRED FOR ACCESSIBLE DOOR PASSAGE SHALL BE MOUNTED NO HIGHER THAN 48" ABOVE FINISHED FLOOR.
 4. THE MAX PULL/PUSH EFFORT TO OPERATE DOORS SHALL NOT EXCEED 15LBS WITH EFFORT APPLIED AT RIGHT ANGLES TO HINGED DOORS. WHEN FIRE DOORS ARE UTILIZED, THE MAX EFFORT MAY BE INCREASED TO NOT EXCEED 15LBS.
 5. DOOR CLOSER, IF A DOOR HAS A CLOSER, THEN THE SWEEP PERIOD OF THE CLOSER SHALL BE ADJUSTED SO THAT FROM AN OPEN POSITION OF 70 DEGREES, THE DOOR WILL TAKE AT LEAST 3 SECONDS TO MOVE TO A POINT 3 IN (75MM) FROM THE LATCH, MEASURED TO THE LEADING EDGE OF THE DOOR.

- DOOR NOTES :
1. ALL DOOR HARDWARE TO BE ADA / TAS COMPLAINT.
 2. PROVIDE LEVER-STYLE LATCHSETS AND LOCKSETS FOR ALL DOORS WITH SATIN/STAINLESS STEEL FINISH.
 3. INTERIOR GLAZING SHALL BE SINGLE PANE, 1/4" CLEAR TEMPERED GLASS.
 4. THE HARDWARE SETS THAT INCLUDES FINAL CORES - CONTRACTOR TO USE CONSTRUCTION CORE DURING CONSTRUCTION. CONTRACTOR TO CHECK WITH THE OWNER.
 5. FINAL KEYING TO BE PROVIDED BY HARDWARE SUBCONTRACTOR IN COORDINATION WITH THE OWNER.
 6. PROTECT EXISTING WINDOWS DURING CONSTRUCTION AND CLEAN THOROUGHLY BEFORE TURN OVER OF THE PROJECT.

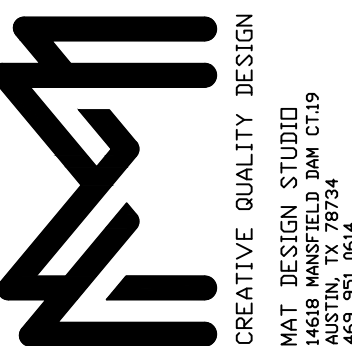

Original Date: 01/12/2024
Issue Log
ISSUED FOR PERMIT: 00/00/2024
ISSUED FOR CONSTRUCTION: 00/00/2024

DRAWN BY: MT
CHECKED BY: MA

© COPYRIGHT

FARM 2 COOK
INTERIOR FINISH-OUT DESIGN
14300 RONALD REAGAN BLVD. BLDG 1
SUITE 102, LEANDER TEXAS 78641

This document, whether in hard copy or electronic format, is copyrighted and an instrument of service to be used in the project for which it was prepared. This document is not to be reproduced or transmitted in any form or by any means, electronic, mechanical, photocopying, recording, or by any information storage and retrieval system, without written permission from MAT Design Studio for the specific purpose intended. In violation of this copyright may result in civil and/or criminal penalties.

Sheet Number: A 4.0
Project Number: 24-036