


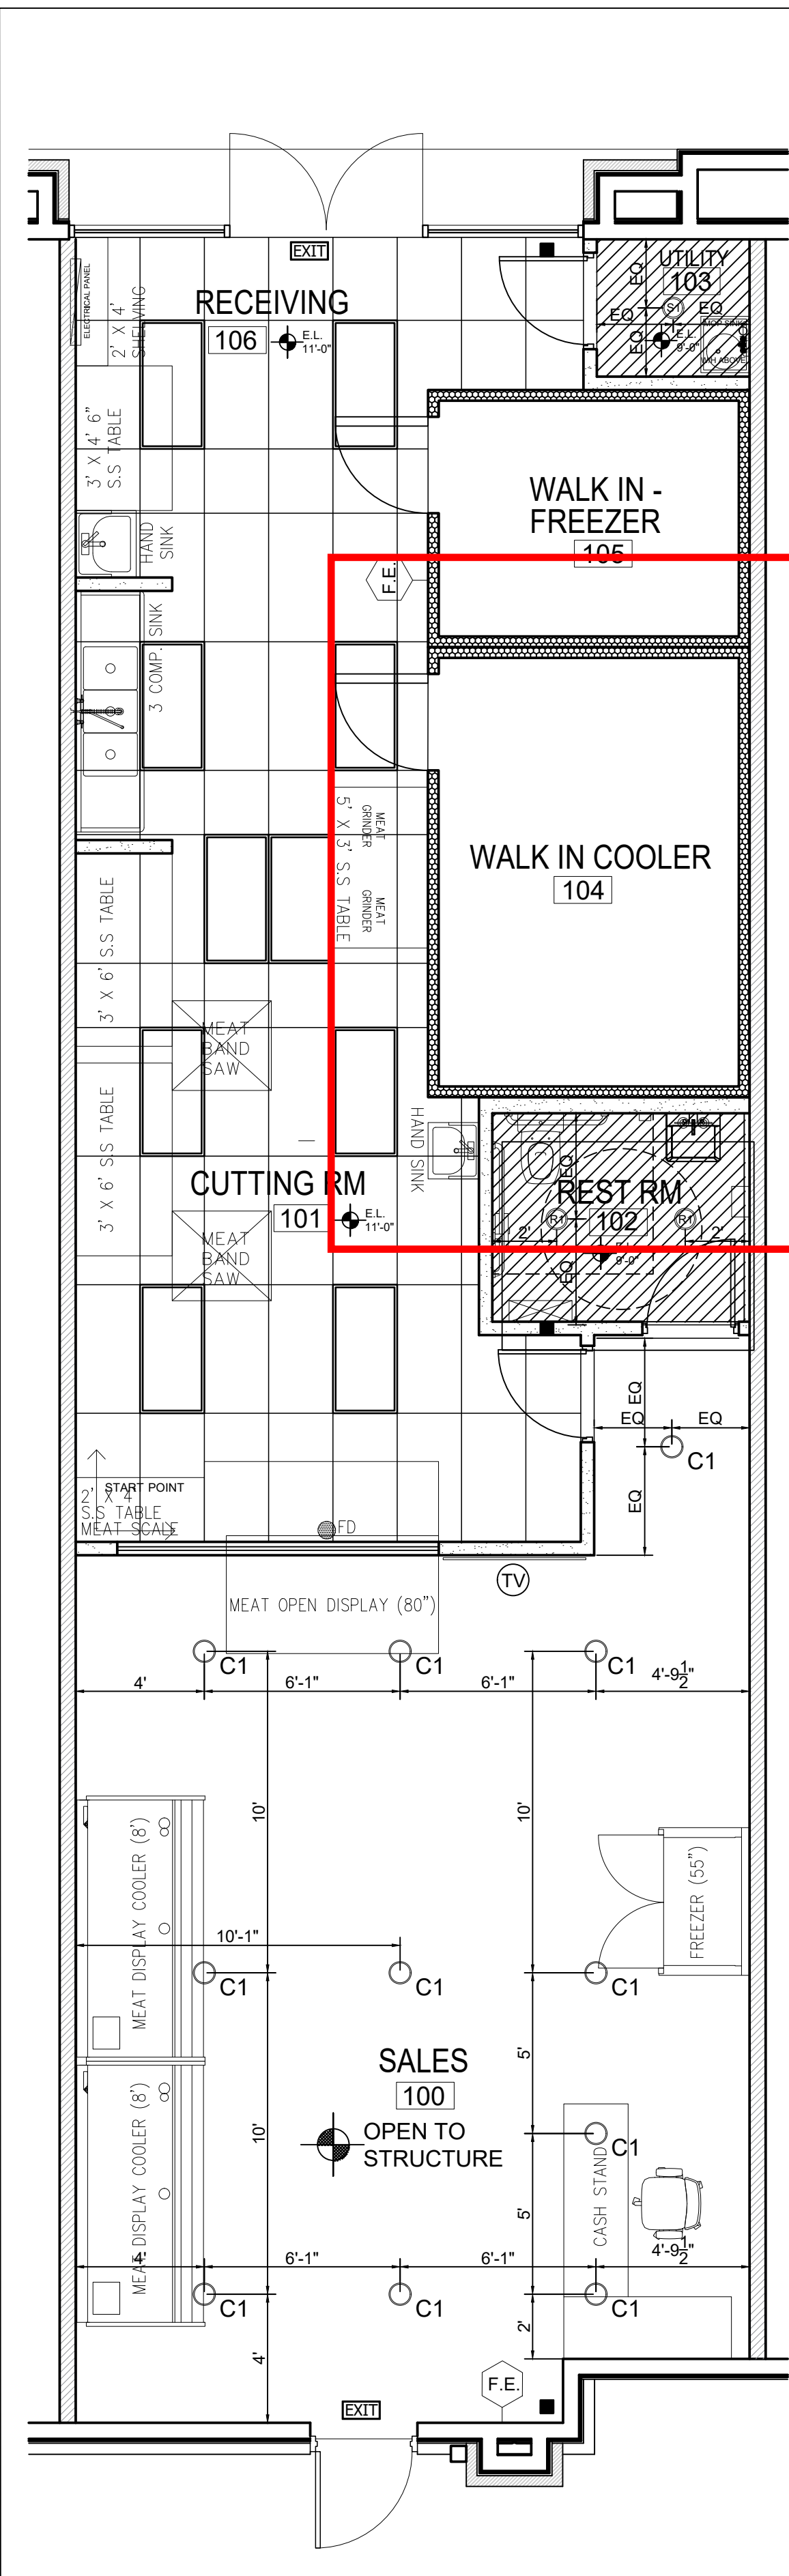

| CEILING LEGEND   |                             |   |
|---|-----------------------------|---|
| TAG   | TYPE                        | SPECIFICATION   |
| (R)   | 5" LED RECESSED DOWNLIGHT   | Lithonia Lighting Model # 5G1BN LED M, 5 in. Brushed Nickel LED Recessed Downlighting Gimbale Module                                                       |
| (FL)   | 7.25" LED FLUSH MOUNT LIGHT | Progress Lighting - P8222 Series 7.25 inch LED Flush Mount - Wet Location Model # P8222-28-30K                                                             |
| (V)   | VANITY LIGHT                | Quoizel Kolt 6" High Brushed Nickel LED Wall Sconce Available at lampsplus, Style # 18C22                                                                  |
| (EXIT)   | ILLUMINATED EXIT SIGN       | REFERENCE ELECTRICAL DRAWINGS FOR DETAILS   |
| (GB)   | GYPSON BOARD                | 5/8" GYPSON BOARD CEILING SEMI GLOSS PAINT, WHITE/level 4 SMOOTH FINISH CEILING HEIGHT AS MENTIONED IN THE ROOMS. PAINT FINISH- REFER ROOM FINISH SCHEDULE |
| (CL)   | CYLINDER LIGHT              | WARELIGHT - 6" LED Architectural Cylinder Light Fixture 2200 Lumens, 25W, CCT Selectable, 120-277V, Black Finish ITEM: WL-CYL6-25W-SCT-0-10V-UNV-S-BK      |
| (L)   | 2' X 4' LAY-IN              | LITHONIA LIGHTING, SERIES 2ESL4, 2' X 4' LED LIGHTING REFERENCE ELECTRICAL DRAWINGS FOR DETAILS                                                            |
| (A)   | OPEN TO STRUCTURE           | OPEN TO STRUCTURE CEILING   |
| GENERAL NOTE:<br>1. CENTER LIGHT FIXTURES IN ROOMS UNLESS NOTED OTHERWISE.<br>2. KEEP HT. OF THE SALES AREA LIGHT FIXTURES AT 9'-0" FROM THE FFL. VERIFY HEIGHTS WITH THE OWNER ALSO.<br>3. KEEP EXTERIOR LIGHT FIXTURES AS IS REPAIR IF NEEDED AND REPLACE LIGHT BULBS IF NEEDED. |                             |   |

| ROOM FINISH LEGEND |                                                                                             |                                          |                               |                |                          |            |   |
|--------------------|---------------------------------------------------------------------------------------------|------------------------------------------|-------------------------------|----------------|--------------------------|------------|---|
| FLOORING AND BASE  |                                                                                             |                                          |                               |                |                          |            |   |
| CODE               | MATERIAL                                                                                    | MANUFACTURER                             | PRODUCT NO.                   | COLOR          | FINISH                   | DIMENSIONS | REMARKS   |
| CT-1               | CERAMIC TILES                                                                               | PIANETTO                                 | SKU: 10089475                 | WHITE          | POLISHED/HIGH GLOSS      | 24"x48"    | - PROVIDE IN SALES RM 100<br>- TILE BASE - WB-1A - TO MATCH WITH FLOOR TILE PROVIDE IN SALES   |
| CT-2               | CEMENTITIOUS URETHANE SEAMLESS FLOORING SYSTEM SAND BROADCAST W/ CONTROL & EXPANSION JOINTS | RES-TEK FLOOR SYSTEMS                    | PUR-GUARD HD-SL               | P-22 DARK GRAY | MATTE SOLID COLOR FINISH | -          | - PROVIDE IN CUTTING RM 101, RECEIVING 106 AND 103<br>- BASE - PUR-GUARD HD-CS COVE BASE TO MATCH W/ FLOORING SYSTEM<br>- RES-TEK Acrylic Flooring & Concrete Repair Solutions<br>- Poron Schmucker Regional Sales Manager, Texas<br>- c: 972.922.6708<br>- e: poron.schmucker@res-tok.net   w: www.res-tok.net<br>- a: 110 Riverside Drive, Cartersville, GA 30120 |
| CT-3               | CERAMIC TILES                                                                               | CORTA GRAY CERAMIC TILE                  | SKU: 100823459                | GRAY           | MATTE                    | 15"x30"    | - PROVIDE IN RESTROOM 102<br>- TILE BASE - WB-3A - TO MATCH WITH WALL TILE PROVIDE IN RESTROOM<br>- TILE GROUT - LATICRETE - STORMY GREY COLOR, PROVIDE ON RESTROOM FLOOR   |
| CEILING            |                                                                                             |                                          |                               |                |                          |            |   |
| CODE               | MATERIAL                                                                                    | MANUFACTURER                             | PRODUCT NO.                   | COLOR          | FINISH                   | DIMENSIONS | REMARKS   |
| REF A4.0           | ACOUSTICAL TILES                                                                            | LAURENTO GRAY II POLISHED PORCELAIN TILE | SKU: 10079883                 | GRAY           | MATTE                    | 24"x24"    | USG, ASTRO ACOUSTICAL PANEL, CLIMA PLUS ITEM NO. 8243, FINE TEXTURED, WHITE SLT SHADOW LINE TEGULAR OR EQUAL. REFER TO REFLECTED CEILING PLAN SHEET - A5.0   |
| REF A4.0           | ACOUSTICAL TILES                                                                            | LAURENTO GRAY II POLISHED PORCELAIN TILE | SKU: 10079883                 | GRAY           | MATTE                    | 24"x24"    | USG, ASTRO ACOUSTICAL PANEL, CLIMA PLUS ITEM NO. 8243, FINE TEXTURED, WHITE SLT SHADOW LINE TEGULAR OR EQUAL. REFER TO REFLECTED CEILING PLAN SHEET - A5.0   |
| REF A4.0           | GYPSON BOARD                                                                                | -                                        | -                             | WHITE          | SEMI GLOSS               | -          | 5/8" GYPSON BD CEILING SEMI GLOSS PAINT WHITE COLOR   |
| REF A4.0           | OPEN TO STRUCTURE                                                                           | -                                        | -                             | -              | -                        | -          | OPEN TO STRUCTURE CEILING IN SALES AREA 100   |
| WALLS              |                                                                                             |                                          |                               |                |                          |            |   |
| CODE               | MATERIAL                                                                                    | MANUFACTURER                             | PRODUCT NO.                   | COLOR          | FINISH                   | DIMENSIONS | REMARKS   |
| PT-1A              | INTERIOR PAINT TYPE 1                                                                       | SHERWIN WILLIAMS                         | PER OWNER                     | PER OWNER      | EGG SHELL                | N/A        | PER OWNER - ON ALL WALLS   |
| PT-1B              | INTERIOR PAINT TYPE 1                                                                       | SHERWIN WILLIAMS                         | PER OWNER                     | PER OWNER      | EGG SHELL                | N/A        | PER OWNER - ON ALL WALLS   |
| CT-1A              | WALL TILE TYPE 1                                                                            | FESTIVAL                                 | BRIGHT WHITE ICE CERAMIC TILE | WHITE          | SMOOTH                   | 4"x10"     | PER OWNER - ON RESTROOM WALLS; REFER SHEET A5.0 FOR ELEVATION HT. AVAILABLE AT FLOOR & DECOR; SKU: 100112689   |
| CT-3A              | WALL TILE TYPE 3                                                                            | ADESSI ASTRID GRIGIO                     | SKU: 100833144                | -              | MATTE                    | 12"x35"    | PER OWNER - ON RESTROOM MAIN WALL ONLY; REFER SHEET A5.0 FOR ELEVATION HT. AVAILABLE AT FLOOR & DECOR; SKU: 100833144   |
| FRP                | FIBER REINFORCED PLASTIC UPTO CEILING                                                       | MARLITE                                  | PEBBLED P145 SILVER           | -              | -                        | -          | IN CUTTING RECEIVING AND UTILITY RM UPTO FINISHED CEILING   |

- NOTES:
1. ALL WALLS SHALL RECEIVE LEVEL 3 SMOOTH DRYWALL FINISH.
  2. ALL PAINT COLOR ARE SUBJECT TO APPROVAL BY THE OWNER AND DESIGN TEAM PRIOR TO APPLICATION. G.C. TO MAKE 2' X 2' MOCK UP FOR APPROVAL.
  3. ALL MATERIALS IN FINISH SCHEDULE ARE CONTRACTOR SUPPLIED UNLESS NOTED OTHERWISE.
  4. CONTRACTOR TO REVIEW AND PRE-APPROVE PAINT COLORS WITH THE OWNER PRIOR TO PURCHASING THEM.
  5. ALL INTERIOR WALLS TO BE SMOOTH DRYWALL WITH EGG-SHELL FINISH. CEILINGS TO HAVE SMOOTH DRYWALL WITH PLAT PAINT FINISH. CONTRACTOR TO REVIEW WALL SHEENS WITH THE OWNER PRIOR TO APPLICATION.
  6. CONTRACTOR TO PROVIDE SUBMITTALS AND (SAMPLING IF POSSIBLE) OF ALL FINISH MATERIALS TO THE OWNER FOR THEIR APPROVAL PRIOR TO ORDERING.

- NOTE: 1. CONTRACTOR TO SHOW THE PAINT MOCK-UP TO THE OWNER AND SEEK APPROVAL PRIOR TO ORDERING AND PERFORMING PAINTWORK.
2. CONTRACTOR TO SHOW THE FLOORING MOCK-UP TO THE OWNER AND SEEK APPROVAL PRIOR TO ORDERING AND INSTALLATION.

