


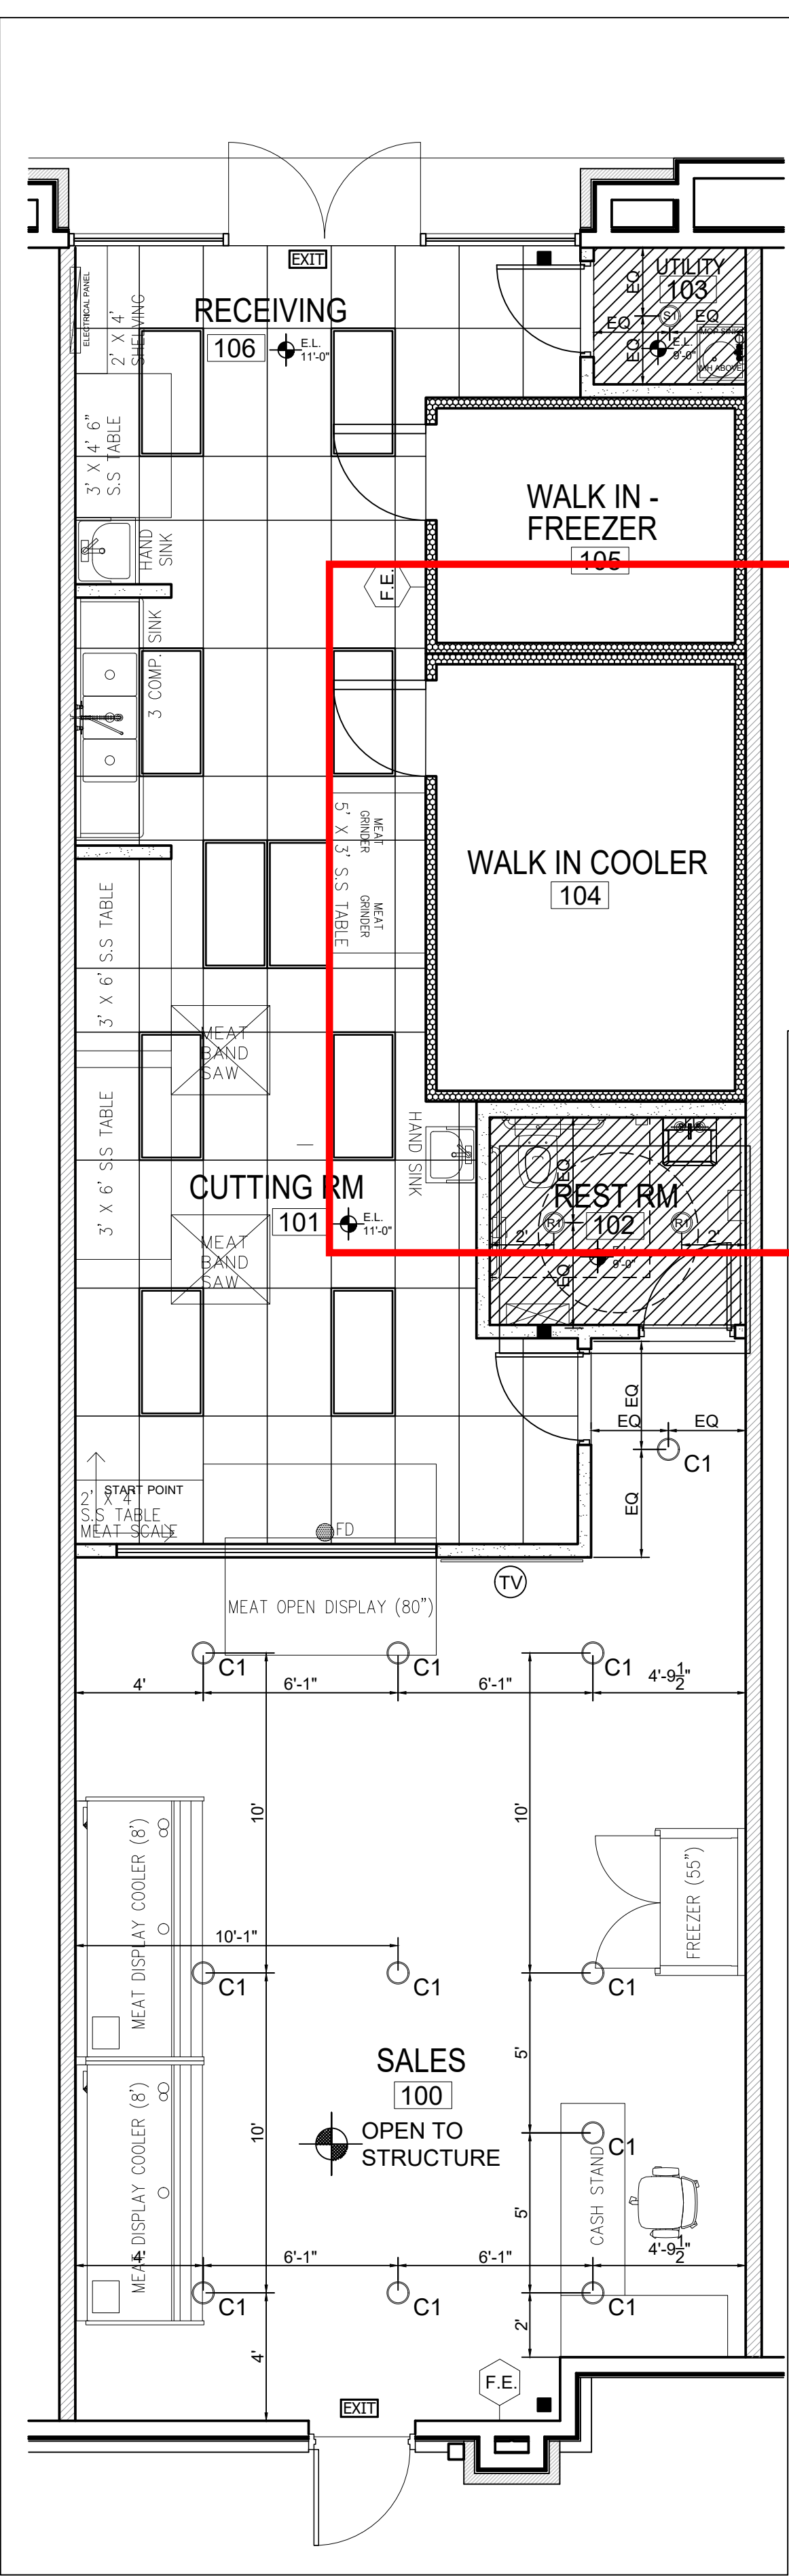

CEILING LEGEND		
TAG	TYPE	SPECIFICATION
(R)	5" LED RECESSED DOWNLIGHT	Lithonia Lighting Model # 5G1BN LED M, 5 in. Brushed Nickel LED Recessed Downlighting Gimbale Module
(S)	7.25" LED FLUSH MOUNTLIGHT	Progress Lighting - P8222 Series 7.25 inch LED Flush Mount - Wet Location Model # P8222-28-30K
(V)	VANITY LIGHT	Quoizel Kolt 6" High Brushed Nickel LED Wall Sconce Available at lampsplus, Style # 18C22
(EXT)	ILLUMINATED EXIT SIGN	REFERENCE ELECTRICAL DRAWINGS FOR DETAILS
(G)	GYPSUM BOARD	5/8" GYPSUM BOARD CEILING SEMI-GLOSS PAINT, WHITE/level 4 SMOOTH FINISH CEILING HEIGHT AS MENTIONED IN THE ROOMS. PAINT FINISH- REFER ROOM FINISH SCHEDULE
(C)	CYLINDER LIGHT	WARELIGHT - 6" LED Architectural Cylinder Light Fixture 2200 Lumens, 25W, CCT Selectable, 120-277V, Black Finish ITEM: WL-CYL6-25W-SCT-0-10V-UNV-S-BK
(L)	2' X 4' LAY-IN	LITHONIA LIGHTING, SERIES 2ESL4, 2' X 4' LED LIGHTING REFERENCE ELECTRICAL DRAWINGS FOR DETAILS
(A)	OPEN TO STRUCTURE	OPEN TO STRUCTURE CEILING

GENERAL NOTE:
1. CENTER LIGHT FIXTURES IN ROOMS UNLESS NOTED OTHERWISE.
2. KEEP HT. OF THE SALES AREA LIGHT FIXTURES AT 9'-0" FROM THE FFL. VERIFY HEIGHTS WITH THE OWNER ALSO.
3. KEEP EXTERIOR LIGHT FIXTURES AS IS REPAIR IF NEEDED AND REPLACE LIGHT BULBS IF NEEDED.

ROOM FINISH LEGEND							
FLOORING AND BASE							
CODE	MATERIAL	MANUFACTURER	PRODUCT NO.	COLOR	FINISH	DIMENSIONS	REMARKS
CT-1	CERAMIC TILES	PIANETTO	SKU: 10089475	WHITE	POLISHED/ HIGH GLOSS	24"x48"	- PROVIDE IN SALES RM 100 - TILE BASE - WB-1A - TO MATCH WITH FLOOR TILE PROVIDE IN SALES
CT-2	CEMENTITIOUS URETHANE SEAMLESS FLOORING SYSTEM SAND BROADCAST W/ CONTROL & EXPANSION JOINTS	RES-TEK FLOOR SYSTEMS	PUR-GUARD HD-SL	P-22 DARK GRAY	MATTE SOLID COLOR FINISH	-	- PROVIDE IN CUTTING RM 101, RECEIVING 106 AND 103 - BASE - PUR-GUARD HD-CS COVE BASE TO MATCH W/ FLOORING SYSTEM - RES-TEK Acrylic Flooring & Concrete Repair Solutions - Poron Schmucker Regional Sales Manager, Texas - c: 972.922.6708 - e: poron.schmucker@res-tok.net w: www.res-tok.net - a: 110 Riverside Drive, Cartersville, GA 30120
CT-3	CERAMIC TILES	CORTA GRAY CERAMIC TILE	SKU: 100823459	GRAY	MATTE	15"x30"	- PROVIDE IN RESTROOM 102 - TILE BASE - WB-3A - TO MATCH WITH WALL TILE PROVIDE IN RESTROOM - TILE GROUT - LATICRETE - STORMY GREY COLOR, PROVIDE ON RESTROOM FLOOR

CEILING							
CODE	MATERIAL	MANUFACTURER	PRODUCT NO.	COLOR	FINISH	DIMENSIONS	REMARKS
REF A4.0	ACOUSTICAL TILES	LAURENTO GRAY II POLISHED PORCELAIN TILE	SKU: 10079883	GRAY	MATTE	24"x24"	USG, ASTRO ACOUSTICAL PANEL, CLIMA PLUS ITEM NO. 8243, FINE TEXTURED, WHITE SLT SHADOW LINE TEGULAR OR EQUAL. REFER TO REFLECTED CEILING PLAN SHEET - A5.0
REF A4.0	ACOUSTICAL TILES	LAURENTO GRAY II POLISHED PORCELAIN TILE	SKU: 10079883	GRAY	MATTE	24"x24"	USG, ASTRO ACOUSTICAL PANEL, CLIMA PLUS ITEM NO. 8243, FINE TEXTURED, WHITE SLT SHADOW LINE TEGULAR OR EQUAL. REFER TO REFLECTED CEILING PLAN SHEET - A5.0
REF A4.0	GYPSUM BOARD	-	-	WHITE	SEMI GLOSS	-	5/8" GYPSUM BD CEILING SEMI-GLOSS PAINT WHITE COLOR
REF A4.0	OPEN TO STRUCTURE	-	-	-	-	-	OPEN TO STRUCTURE CEILING IN SALES AREA 100

WALLS							
CODE	MATERIAL	MANUFACTURER	PRODUCT NO.	COLOR	FINISH	DIMENSIONS	REMARKS
PT-1A	INTERIOR PAINT TYPE 1	SHERWIN WILLIAMS	PER OWNER	PER OWNER	EGG SHELL	N/A	PER OWNER - ON ALL WALLS
PT-1B	INTERIOR PAINT TYPE 1	SHERWIN WILLIAMS	PER OWNER	PER OWNER	EGG SHELL	N/A	PER OWNER - ON ALL WALLS
CT-1A	WALL TILE TYPE 1	FESTIVAL	BRIGHT WHITE ICE CERAMIC TILE	WHITE	SMOOTH	4"x10"	PER OWNER - ON RESTROOM WALLS; REFER SHEET A5.0 FOR ELEVATION HT. AVAILABLE AT FLOOR & DECOR; SKU: 100112689
CT-3A	WALL TILE TYPE 3	ADESSI ASTRID GRIGIO	SKU: 100833144	-	MATTE	12"x35"	PER OWNER - ON RESTROOM MAIN WALL ONLY; REFER SHEET A5.0 FOR ELEVATION HT. AVAILABLE AT FLOOR & DECOR; SKU: 100833144
FRP	FIBER REINFORCED PLASTIC UPTO CEILING	MARLITE	PEBBLED P145 SILVER	-	-	-	IN CUTTING RECEIVING AND UTILITY RM UPTO FINISHED CEILING

- NOTES:
1. ALL WALLS SHALL RECEIVE LEVEL 3 SMOOTH DRYWALL FINISH.
 2. ALL PAINT COLOR ARE SUBJECT TO APPROVAL BY THE OWNER AND DESIGN TEAM PRIOR TO APPLICATION. G.C. TO MAKE 2' X 2' MOCK UP FOR APPROVAL.
 3. ALL MATERIALS IN FINISH SCHEDULE ARE CONTRACTOR SUPPLIED UNLESS NOTED OTHERWISE.
 4. CONTRACTOR TO REVIEW AND PRE-APPROVE PAINT COLORS WITH THE OWNER PRIOR TO PURCHASING THEM.
 5. ALL INTERIOR WALLS TO BE SMOOTH DRYWALL WITH EGG-SHELL FINISH. CEILINGS TO HAVE SMOOTH DRYWALL WITH FLAT PAINT FINISH. CONTRACTOR TO REVIEW WALL SHEENS WITH THE OWNER PRIOR TO APPLICATION.
 6. CONTRACTOR TO PROVIDE SUBMITTALS AND (SAMPLING IF POSSIBLE) OF ALL FINISH MATERIALS TO THE OWNER FOR THEIR APPROVAL PRIOR TO ORDERING.
- NOTE: 1. CONTRACTOR TO SHOW THE PAINT MOCK-UP TO THE OWNER AND SEEK APPROVAL PRIOR TO ORDERING AND PERFORMING PAINTWORK.
2. CONTRACTOR TO SHOW THE FLOORING MOCK-UP TO THE OWNER AND SEEK APPROVAL PRIOR TO ORDERING AND INSTALLATION.

